


ELYENAI
DAMATTA

**PORT
FÓLIO**

DESIGN DE INTERIORES E ARQUITETURA

D E S I G N E R D E I N T E R I O R E S

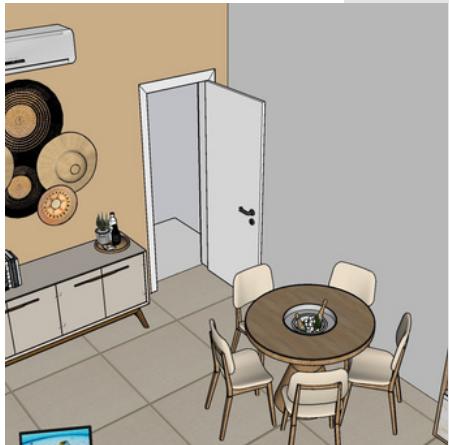

ELYENAI C.
DA MATTA



F O R M A D A E M 2 0 1 5 E M
D E S I G N D E I N T E R I O R E S
P E L O C E S / J F

Mai Da Matta
INTERIOR DESIGN



Projeto Área Gourmet

Nai DaMatta
INTERIOR DESIGN




Projeto Home Office

Nai DaMatta
INTERIOR DESIGN



Projeto Home Office Executado

Nai DaMatta
INTERIOR DESIGN

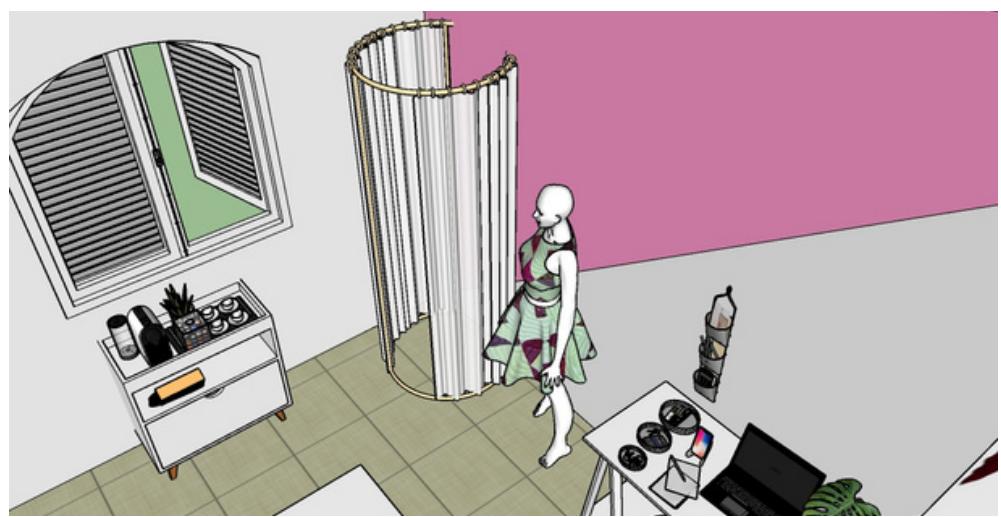



Projeto Loja Flor Plus

Nai Da Matta
INTERIOR DESIGN



Projeto Redecoração Residencial

Nai DaMatta
INTERIOR DESIGN

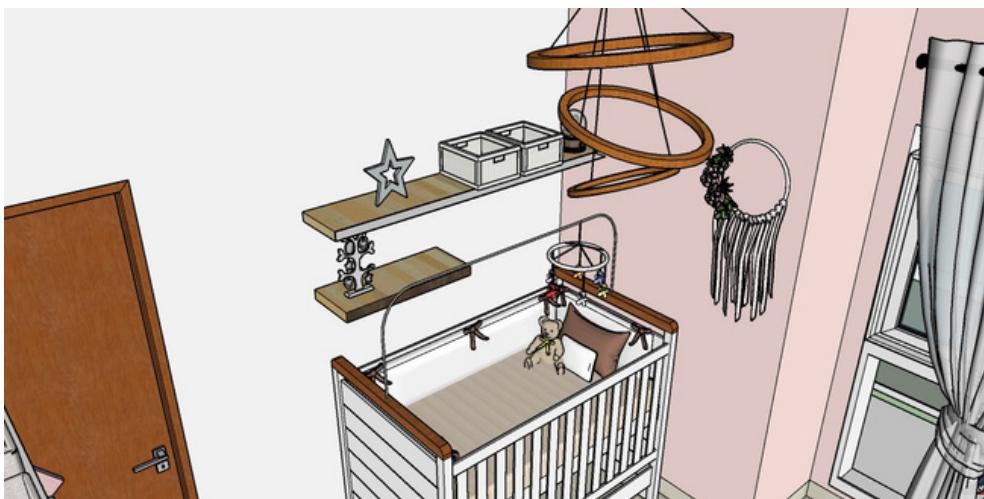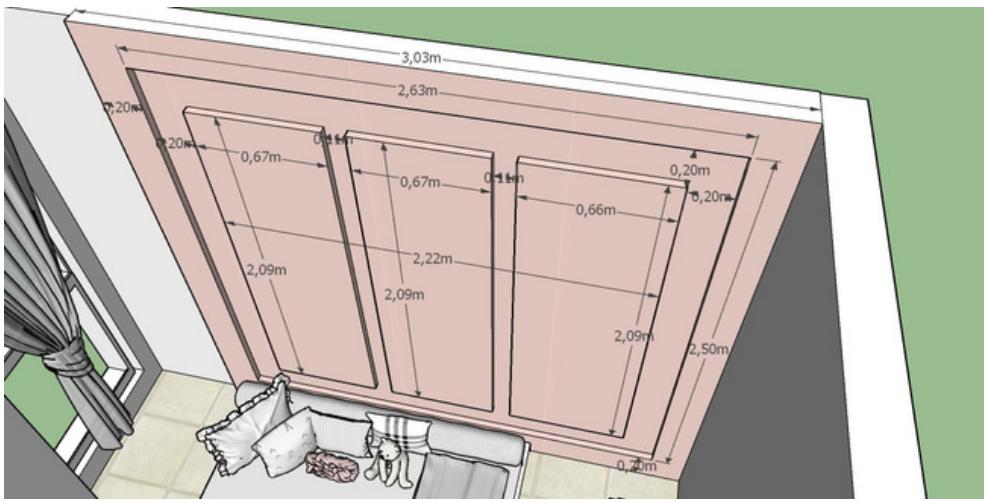

Projeto Quarto de 2 meninas

Nai Da Matta
INTERIOR DESIGN




Projeto Redecoração Residencial

Nai DaMatta
INTERIOR DESIGN



Projeto Vitrine da Loja Coccinela

Nai Da Matta
INTERIOR DESIGN

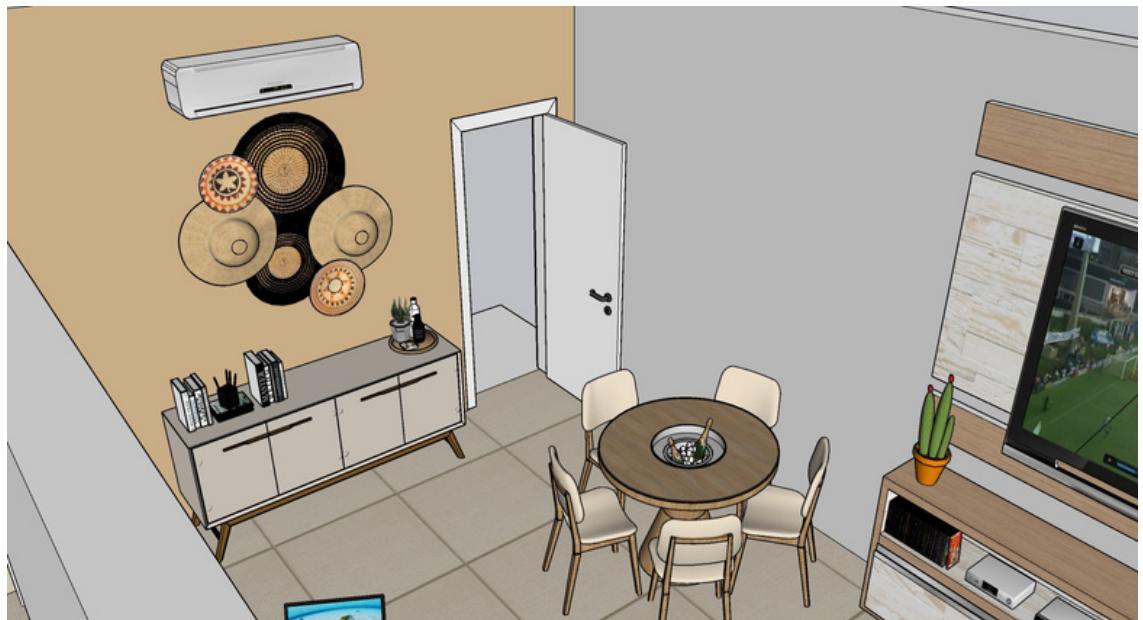

Projeto Redecoração Residencial

Nai DaMatta
INTERIOR DESIGN



Projeto Fachada Residencial

Nai DaMatta
INTERIOR DESIGN



Projeto Cozinha Residencial


Nai DaMatta
INTERIOR DESIGN



Projeto Apto MRV

Nai DaMatta

INTERIOR DESIGN

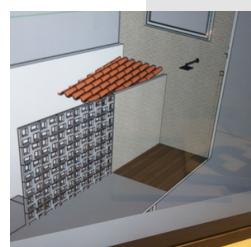



Elyenai C. da Matta




Estudante de Arquitetura
Iniciei em Março de 2020
na Universidade Estácio
de Sá.

Migrei para a Universidade
UNINTER em Fevereiro de
2022.


A R Q U I T E T U R A

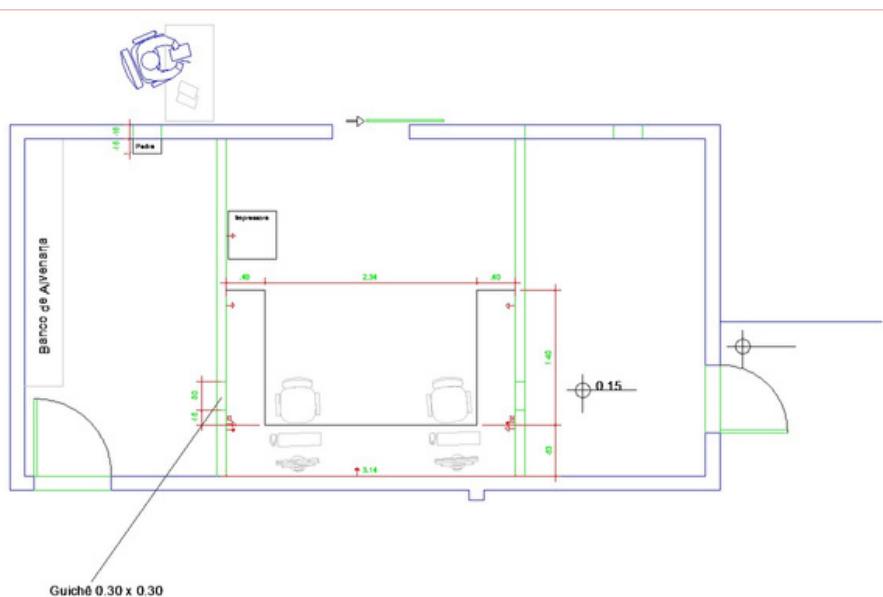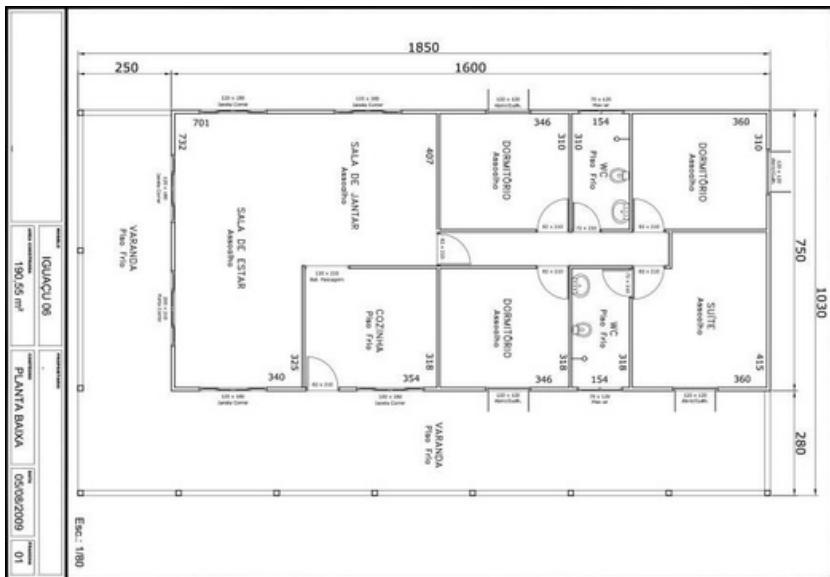


Trabalhos da Faculdade de Arquitetura

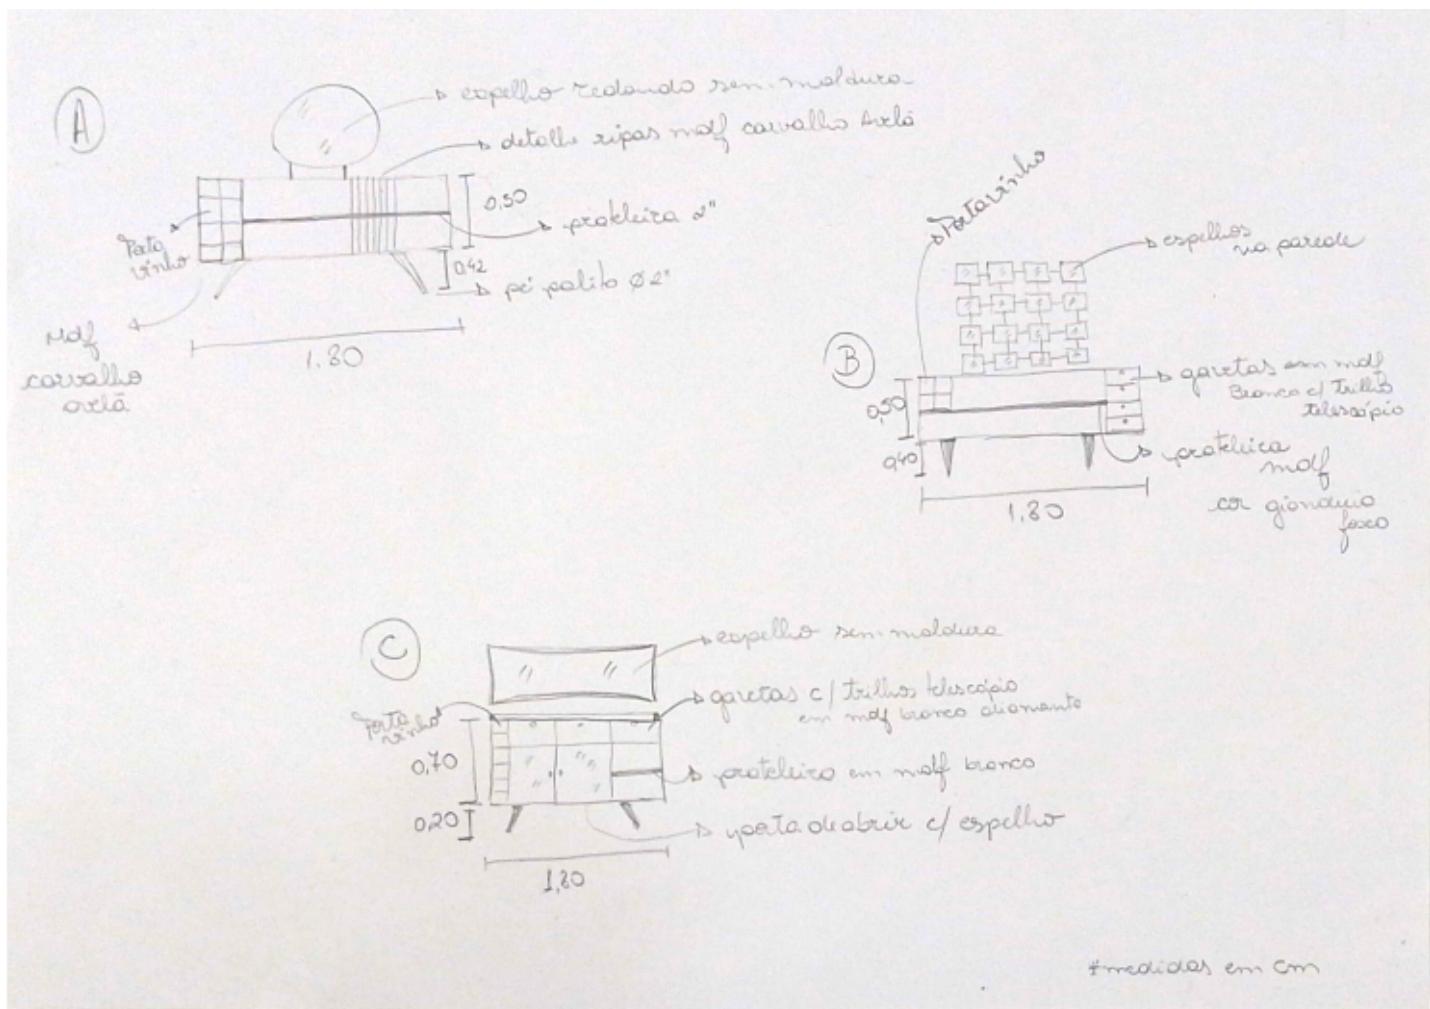

Trabalhos da Faculdade de Arquitetura

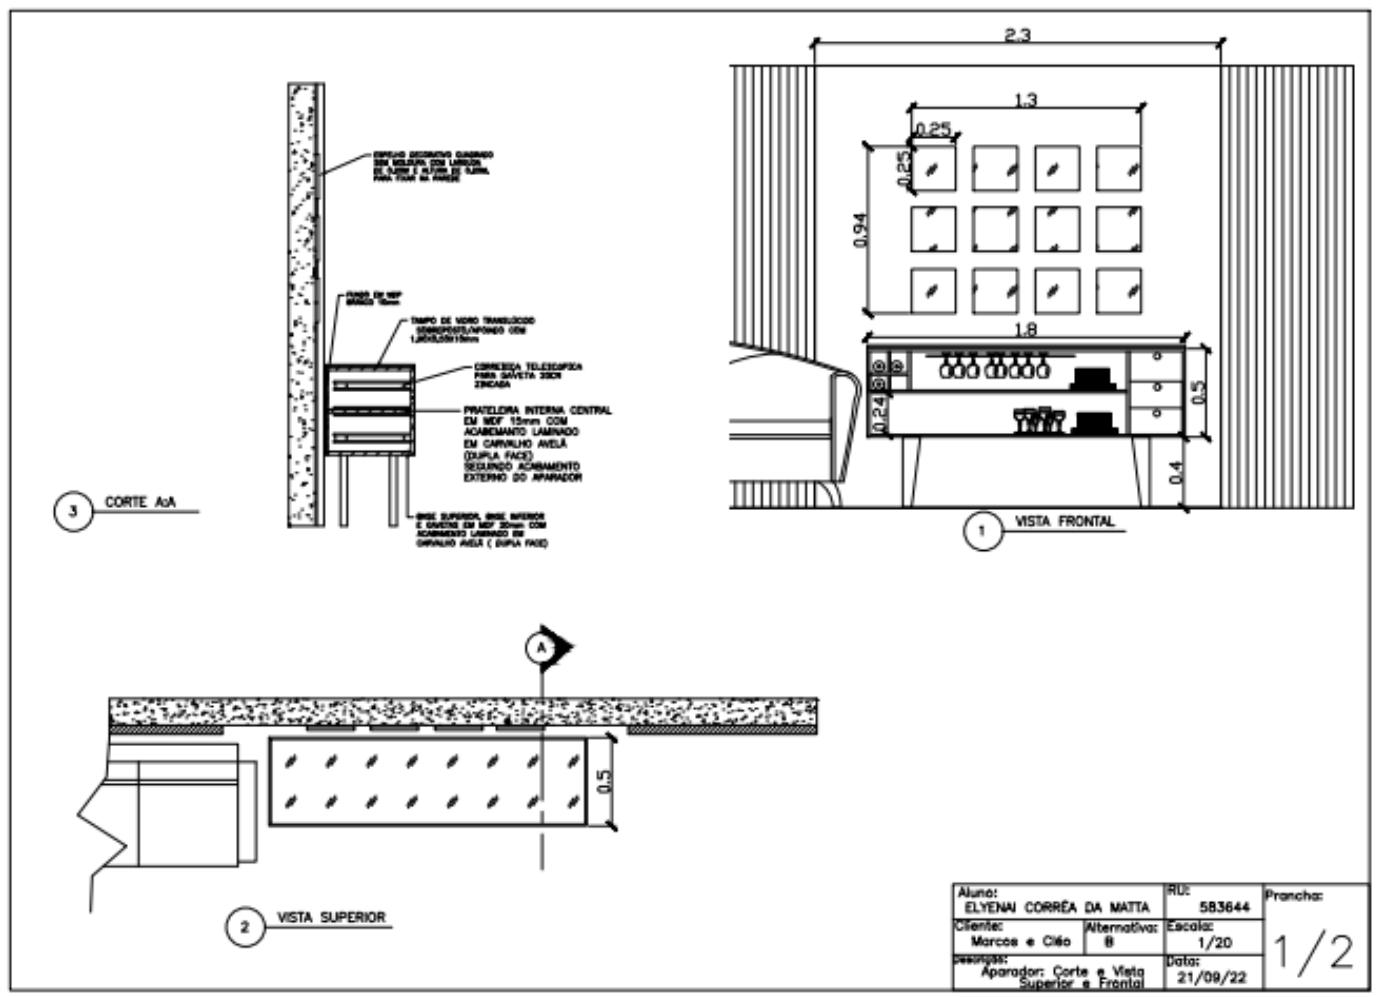

Criação de Mobiliário feito na faculdade de Arquitetura

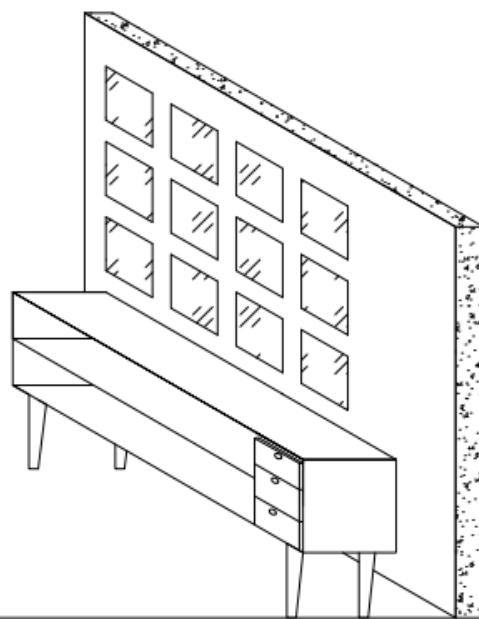



4 Perspectiva Isométrica

Aluno:	ELYENAI CORRÉA DA MATTA	RU:	583644	Prancha:
Cliente:	Marcos e Cléo	Alternativa:	B	Escala: 1/20
Descrição:	Aparador: Perspectiva Isométrica	Data:	21/09/22	2/2

Criação de Móveis feito na faculdade de Arquitetura






Maquete elaborada na faculdade Arquitetura

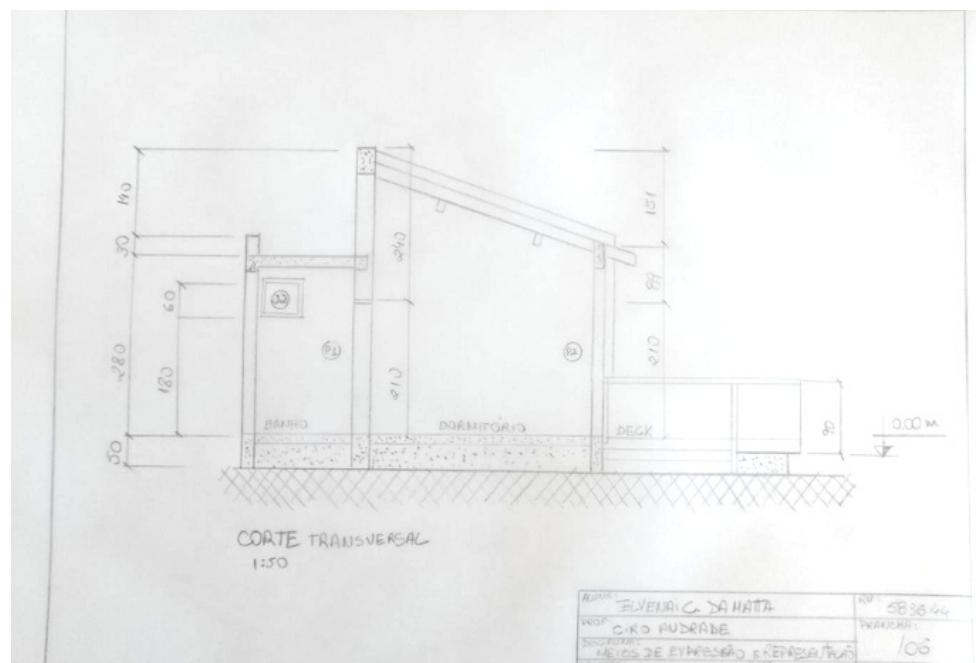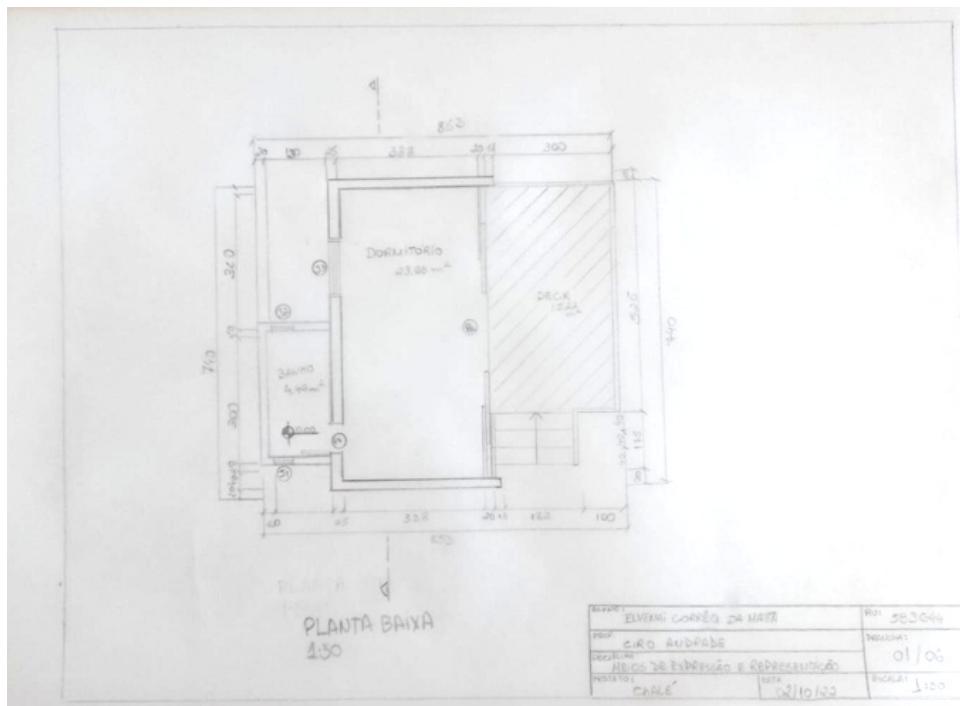


Planta da maquete elaborada na Faculdade Arquitetura

ESTÁGIO DE ARQUITETURA

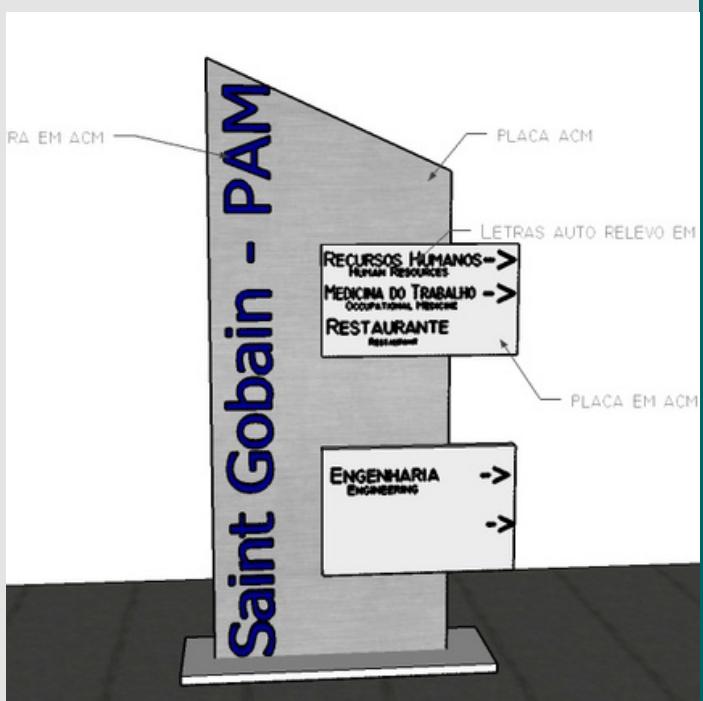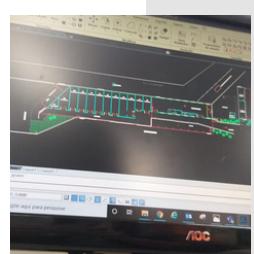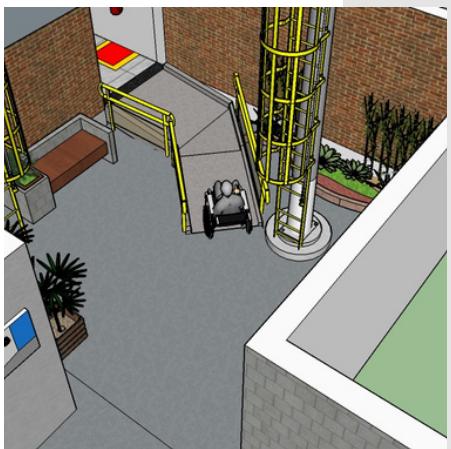


PROJETOS
REALIZADOS NO
ESTÁGIO DE
ARQUITETURA

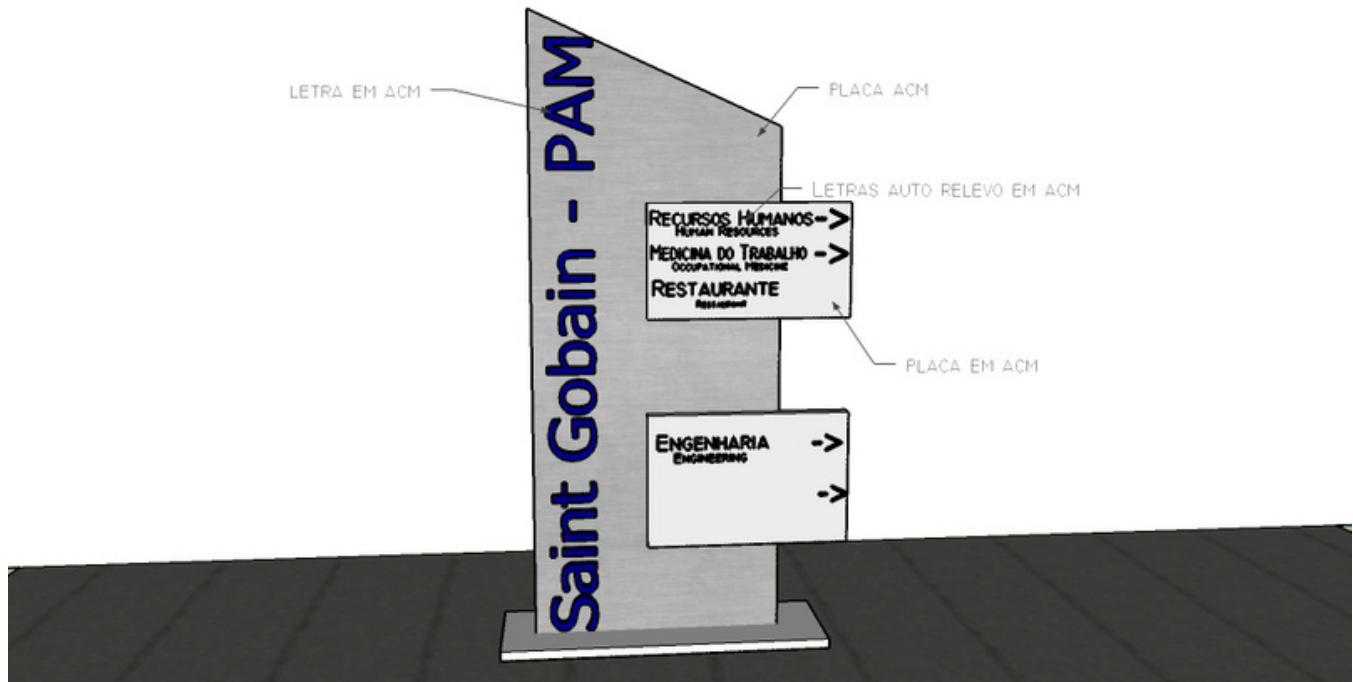

Projeto Modernização de Totem

Nai DaMatta

INTERIOR DESIGN

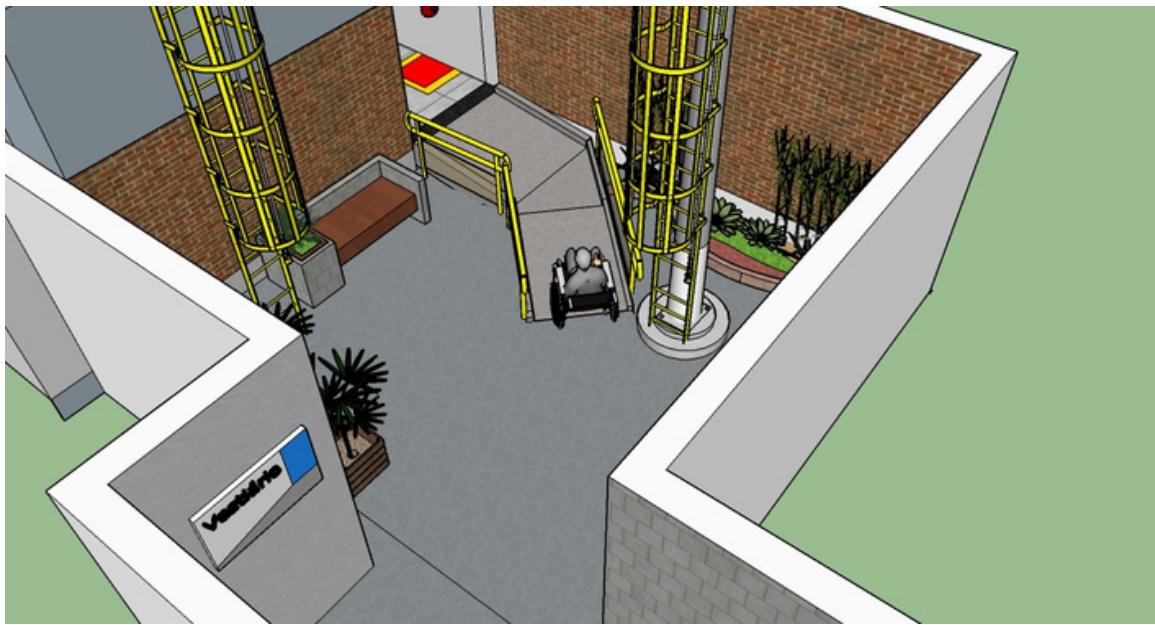

Projeto Área externa de Vestiário

Nai DaMatta
INTERIOR DESIGN



Projeto Revitalização do Escritório

Nai DaMatta
INTERIOR DESIGN



Projeto Escritório no Contêiner


O termo contêiner ou contentor é um equipamento utilizado para transportar carga.

Nai DaMatta
INTERIOR DESIGN



Projeto Retrofit do Setor de RH

Nai DaMatta
INTERIOR DESIGN

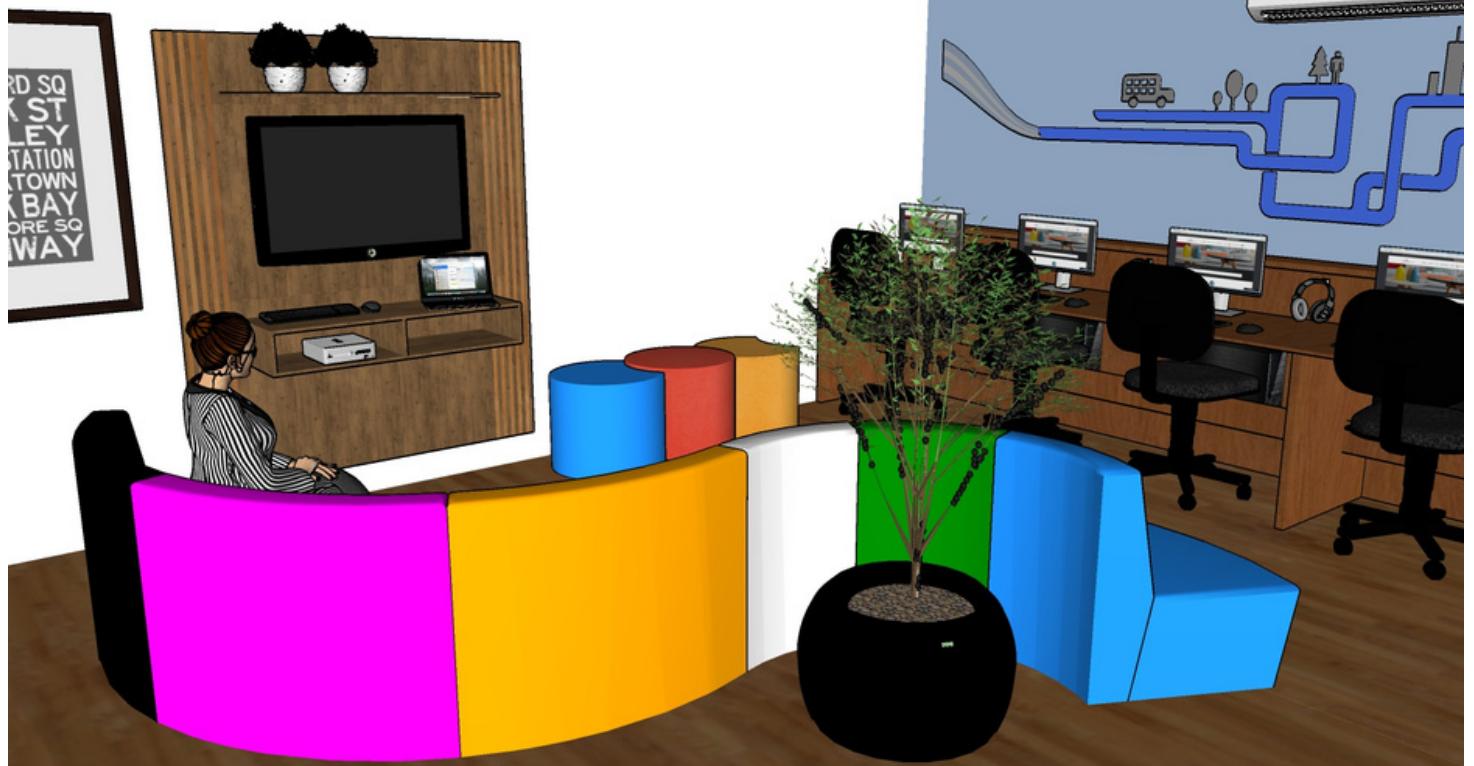

Projeto Reforma na Sala Digital

Nai DaMatta
INTERIOR DESIGN